


Anschlussschema · VDM10 LAN/PoE

Netzwerk-Variante: Türstation und Innenstationen per Netzkabel am PoE-Switch · Router für die App · Türöffner mit eigenem Netzteil

VDM10 2.0 · ADM10

LAN / PoE

[Zum Produkt ↗](#)

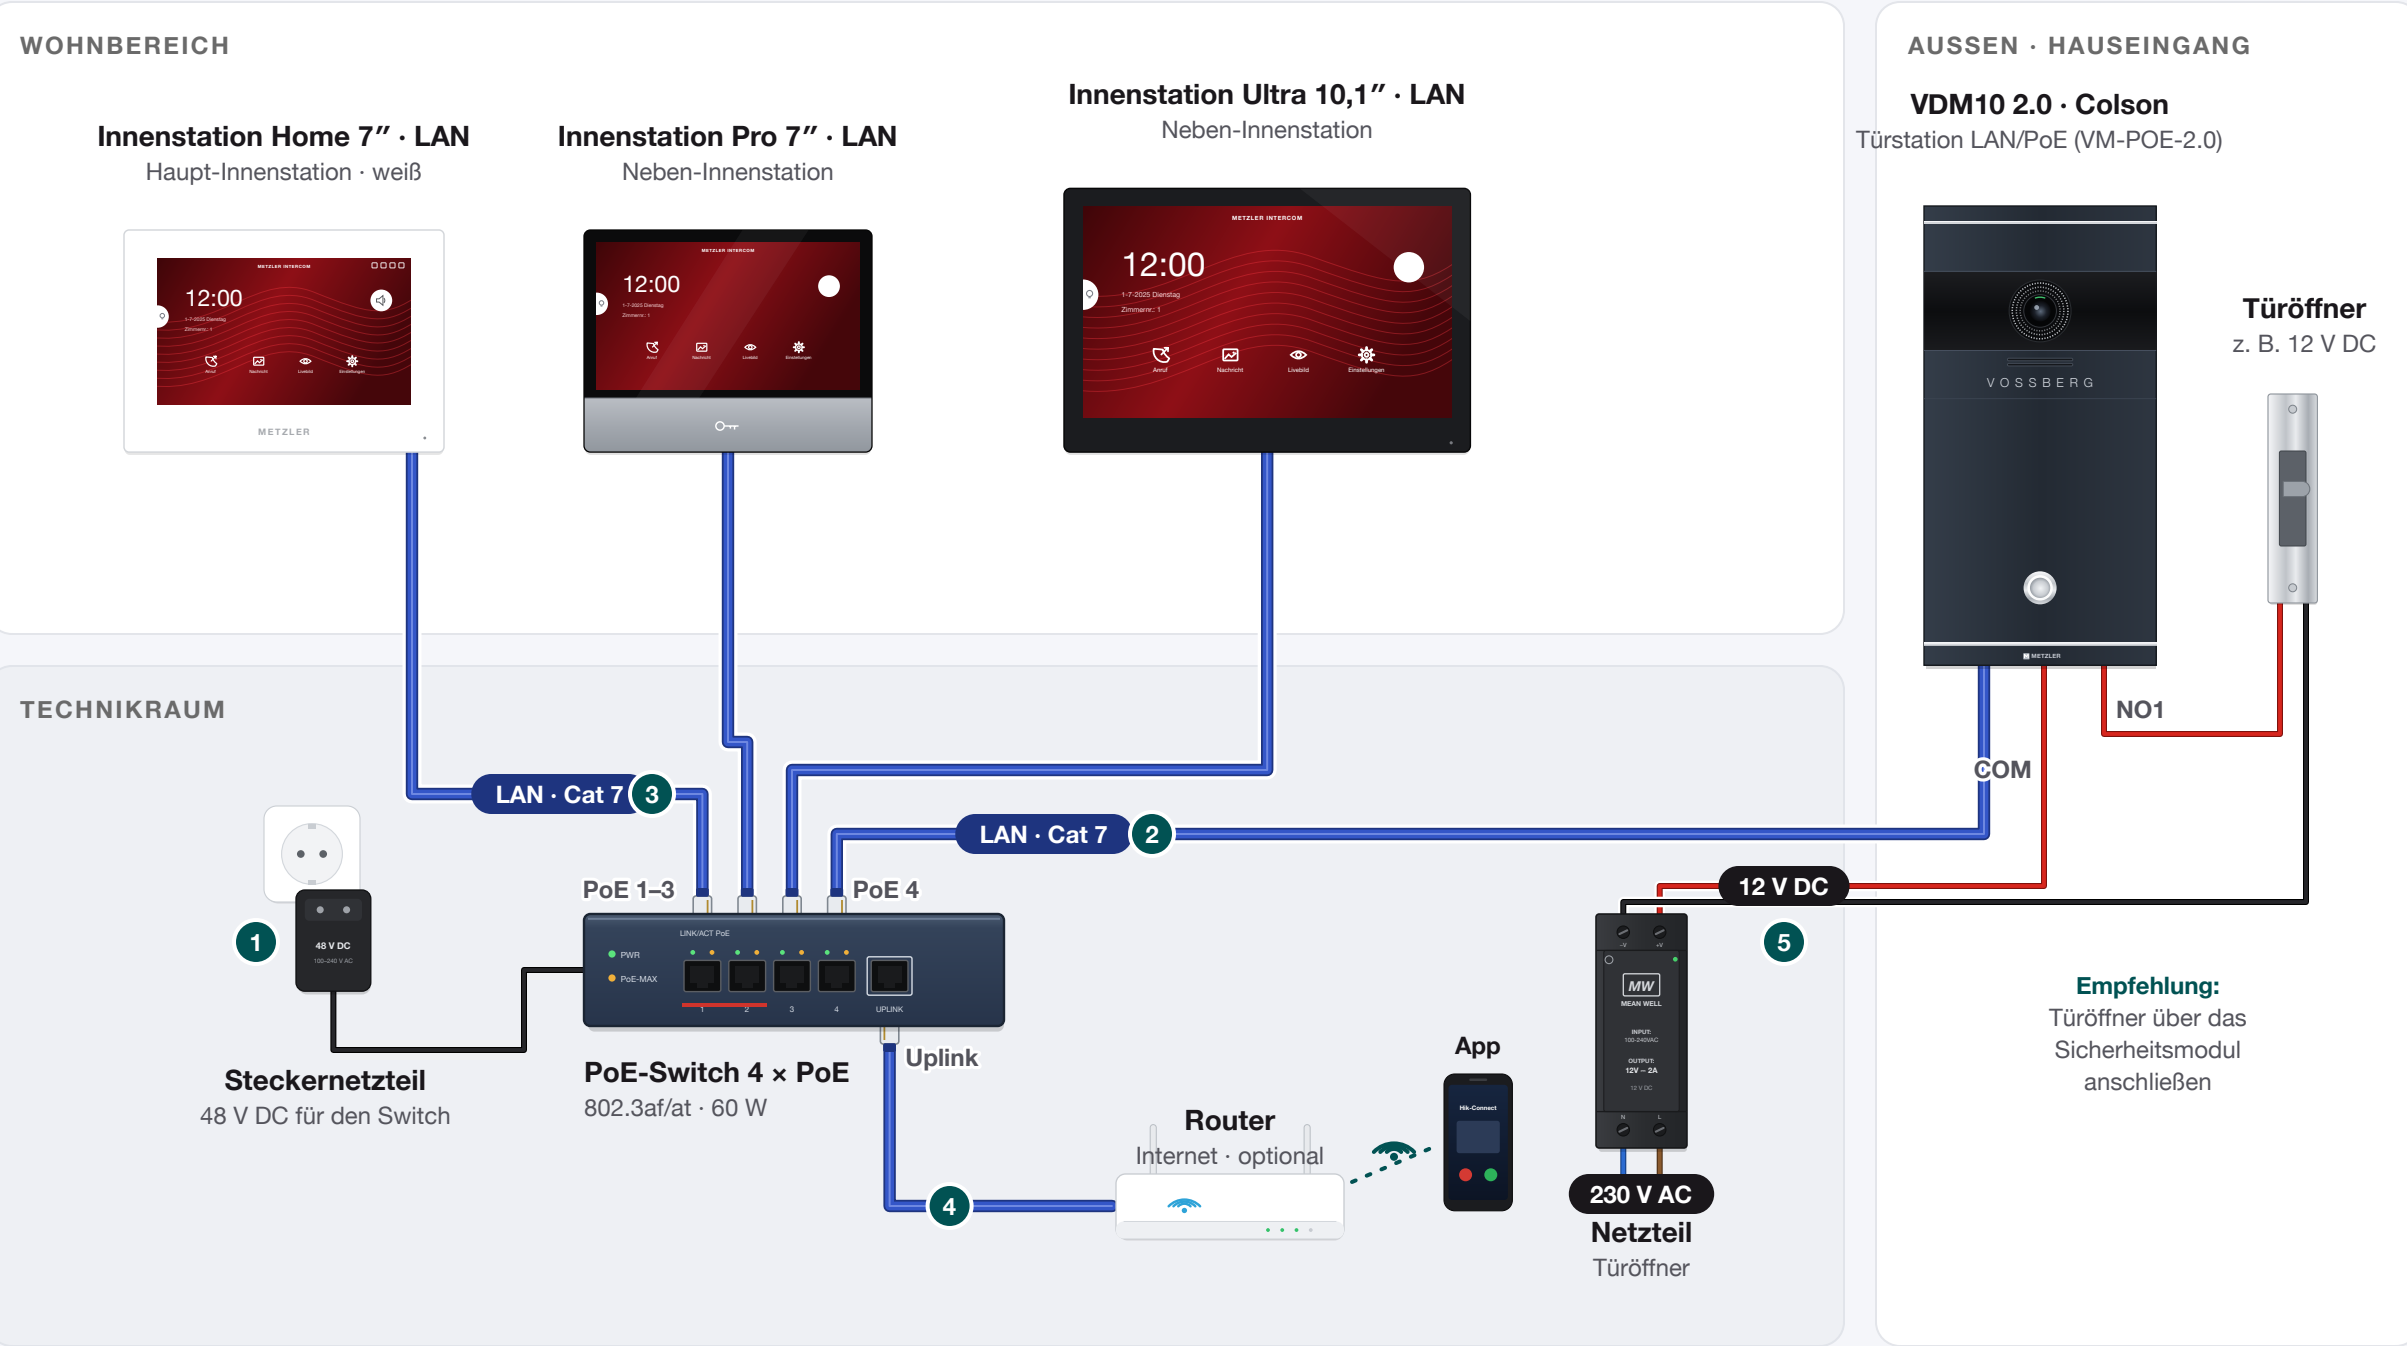

So wird angeschlossen

- 1 PoE-Switch über das Steckernetzteil (48 V DC) mit Strom versorgen.
- 2 Türstation (LAN/PoE) mit Netzkabel an einen PoE-Port anschließen.
- 3 Jede Innenstation mit eigenem Netzkabel an einen PoE-Port (IEEE 802.3af).
- 4 Uplink-Port mit dem Router verbinden – für App und Einrichtung per PC.
- 5 Türöffner: COM → Netzteil (+), NO1 → Türöffner, Türöffner → Netzteil (-).

Wichtig

- Netzkabel CAT5e bis 60 m, ab CAT6 bis 100 m; an jedem Anschluss 1,5–2 m Reserve lassen und beschriften.
- Türöffner mit separater Leitung und eigenem Netzteil (Relais max. 30 V / 1 A).
- Innenstation nicht gleichzeitig per LAN und WLAN mit demselben Router verbinden.
- Ohne PoE: Home/Ultra über Netzteil 12 V (3 m Kabel) versorgen – nicht für Pro.
- 230-V-Leitungen ≥ 0,5 m entfernt verlegen. Gilt auch für ADM10 (Audio).

Leitungen

- Netzkabel Cat 5e–7 mit RJ45 (Daten + PoE)
- 12 / 48 V DC · rot = +, schwarz = –
- 230 V AC · L braun, N blau (Elektrofachkraft)
- Internet / WLAN zur Hik-Connect App