


Anschlussschema · XDM10 Einfamilienhaus

2-Draht-BUS über vorhandene Klingelleitung · 2 Innenstationen in Reihe · Türöffner über Sicherheitsmodul

XDM10

2-Draht-BUS · 48 V

[Zum Produkt ↗](#)

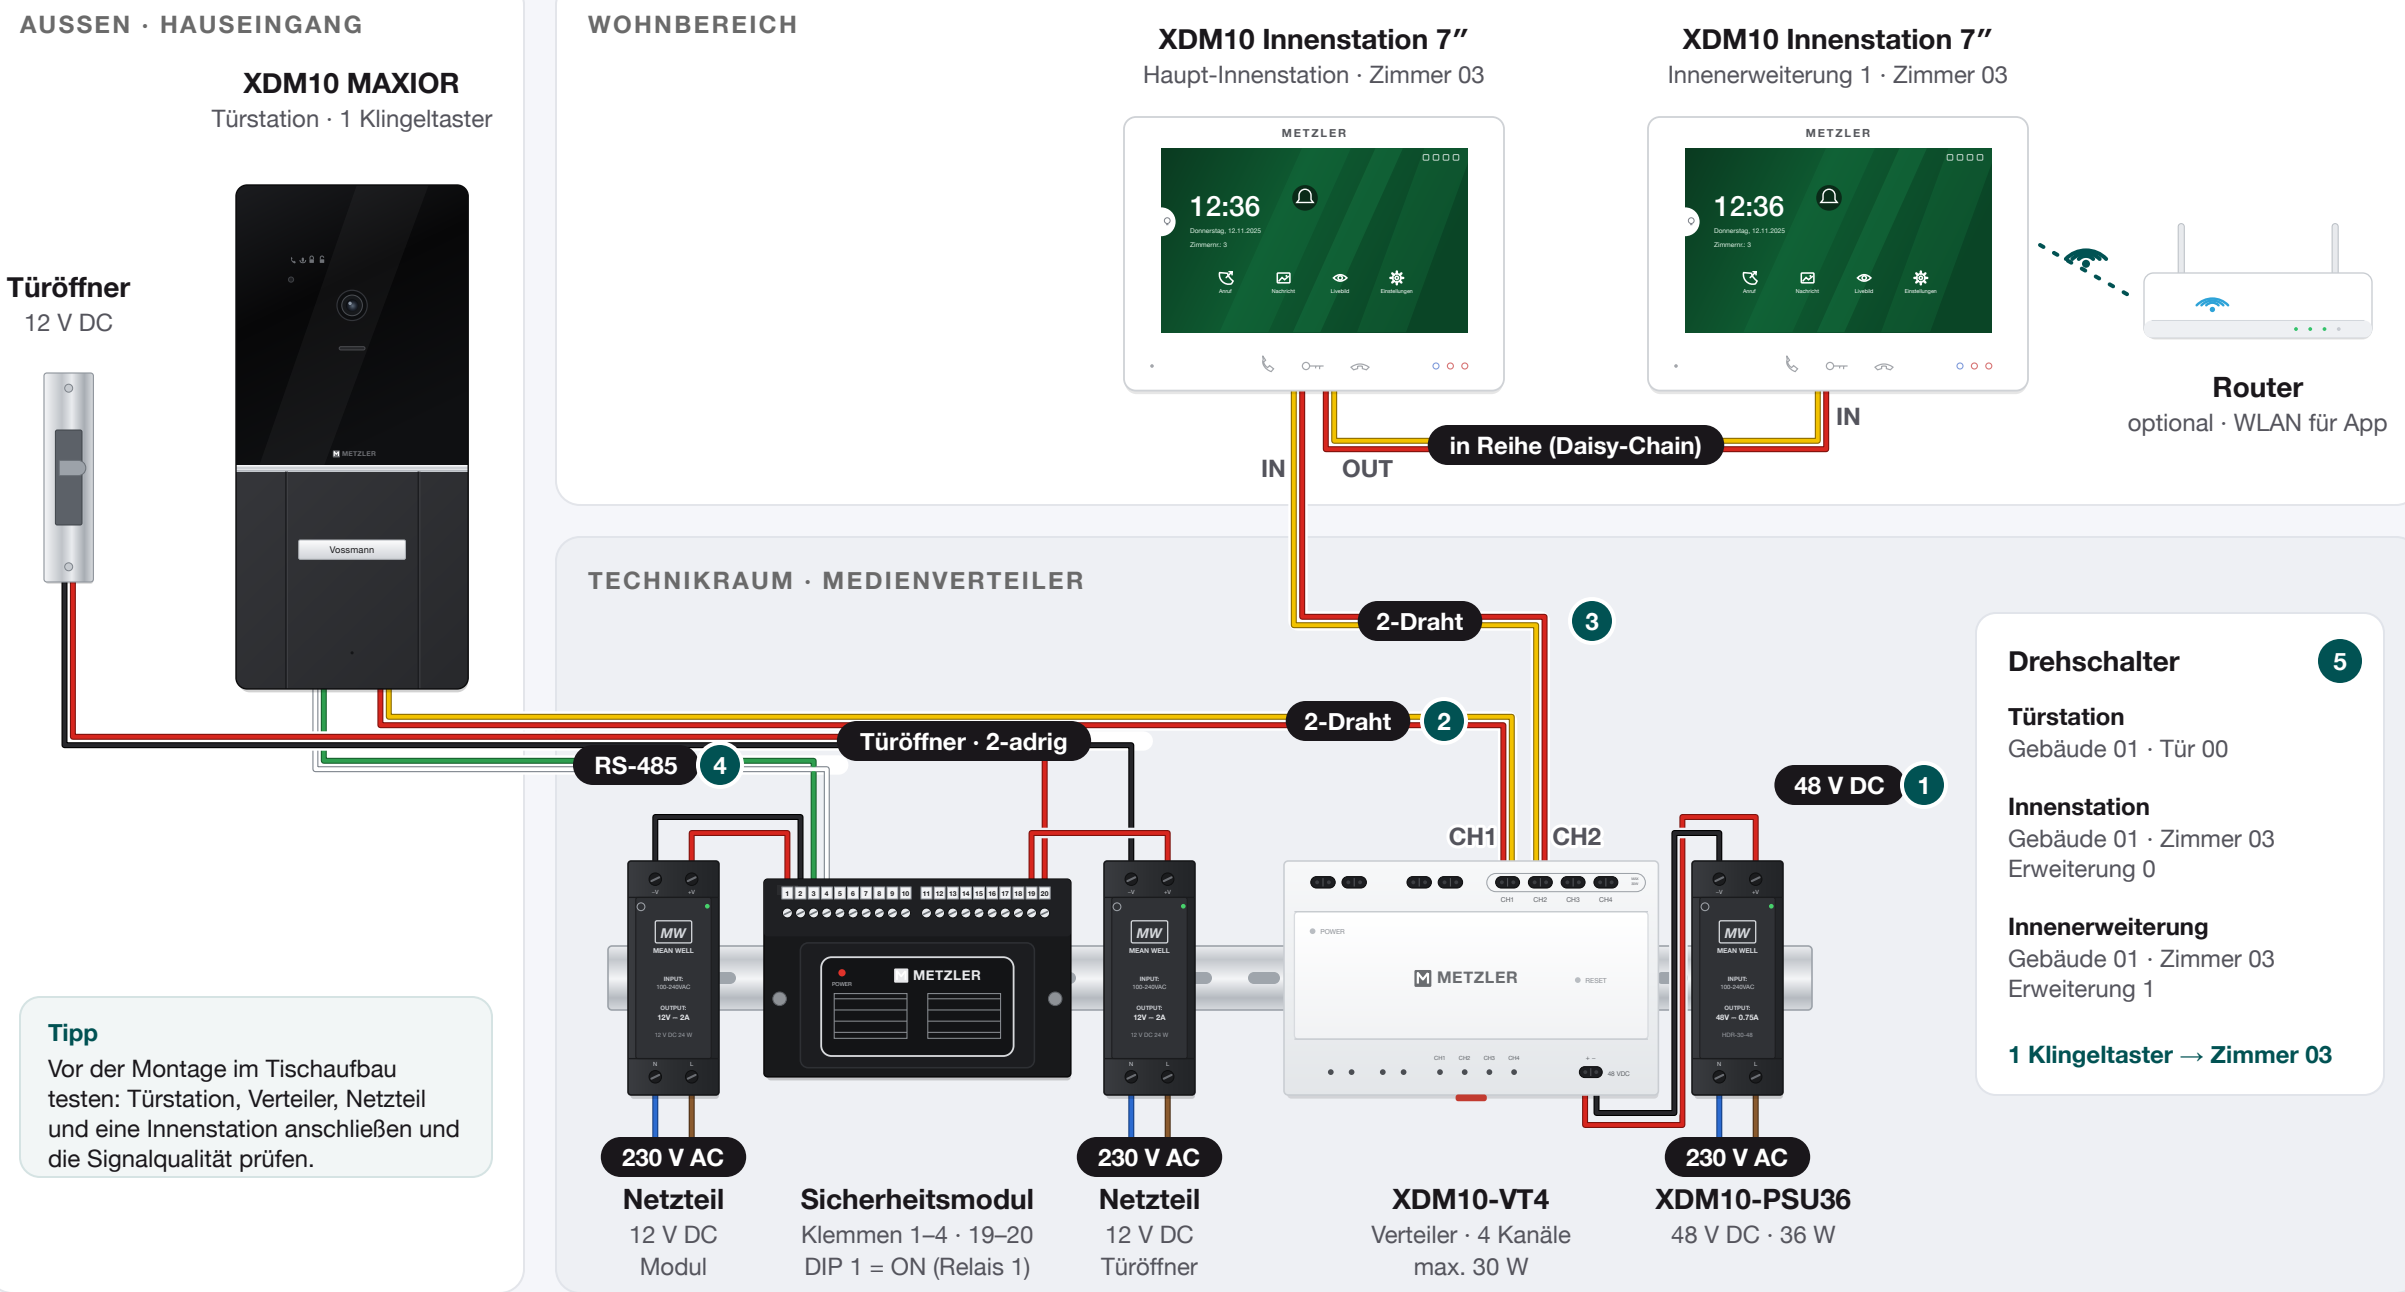

So wird angeschlossen

- 1 Netzteil XDM10-PSU36 an 230 V anschließen und mit „+ – 48 VDC“ am Verteiler verbinden.
- 2 Türstation mit einem freien Kanal CH1–CH4 verbinden (eigenes Aderpaar).
- 3 Haupt-Innenstation an CH2 (Klemme 2-Draht-IN), Innenerweiterung von OUT → IN in Reihe.
- 4 Sicherheitsmodul: RS-485 an Klemme 3/4, eigenes 12-V-Netzteil an 1/2, Türöffner an 19/20.
- 5 Drehschalter einstellen (Gebäude-Nr., Zimmer-Nr.), Kopplung starten – fertig.

Wichtig

- Pro Gerät nur ein Aderpaar nutzen, keine Netzkabel (Impedanz über 42 Ω / 100 m).
- Leitungslängen: Verteiler → Türstation ≤ 60 m; Verteiler → Innenstation ≤ 60 m (Twisted Pair ≤ 40 m); Innenstation → Innenstation ≤ 100 m (Twisted Pair ≤ 80 m).
- Ein PSU36 versorgt 1 Türstation und bis zu 4 Innenstationen; max. 4 Innenstationen in Reihe.
- 230-V-Leitungen ≥ 0,5 m entfernt verlegen. XDM10 ist nicht mit VDM10 2-Draht mischbar.
- Zuerst das Sicherheitsmodul, dann die Sprechanlage einschalten. Nur Türöffner mit 12 V DC.

Leitungen

- 2-Draht-BUS – 1 Aderpaar, z. B. J-Y(St)Y 2×2×0,8
- RS-485 Türstation → Sicherheitsmodul
- 12 / 48 V DC · rot = +, schwarz = –
- 230 V AC · L braun, N blau (Elektrofachkraft)
- WLAN (optional) für die Hik-Connect App