


Anschlussschema · XDM10 Mehrfamilienhaus

2-Draht-BUS mit Stockwerksverteiler · 3 Wohnungen · mehr als 4 Innenstationen möglich (Set „8 Anschlüsse“)

XDM10

2-Draht-BUS · 48 V

[Zum Produkt ↗](#)

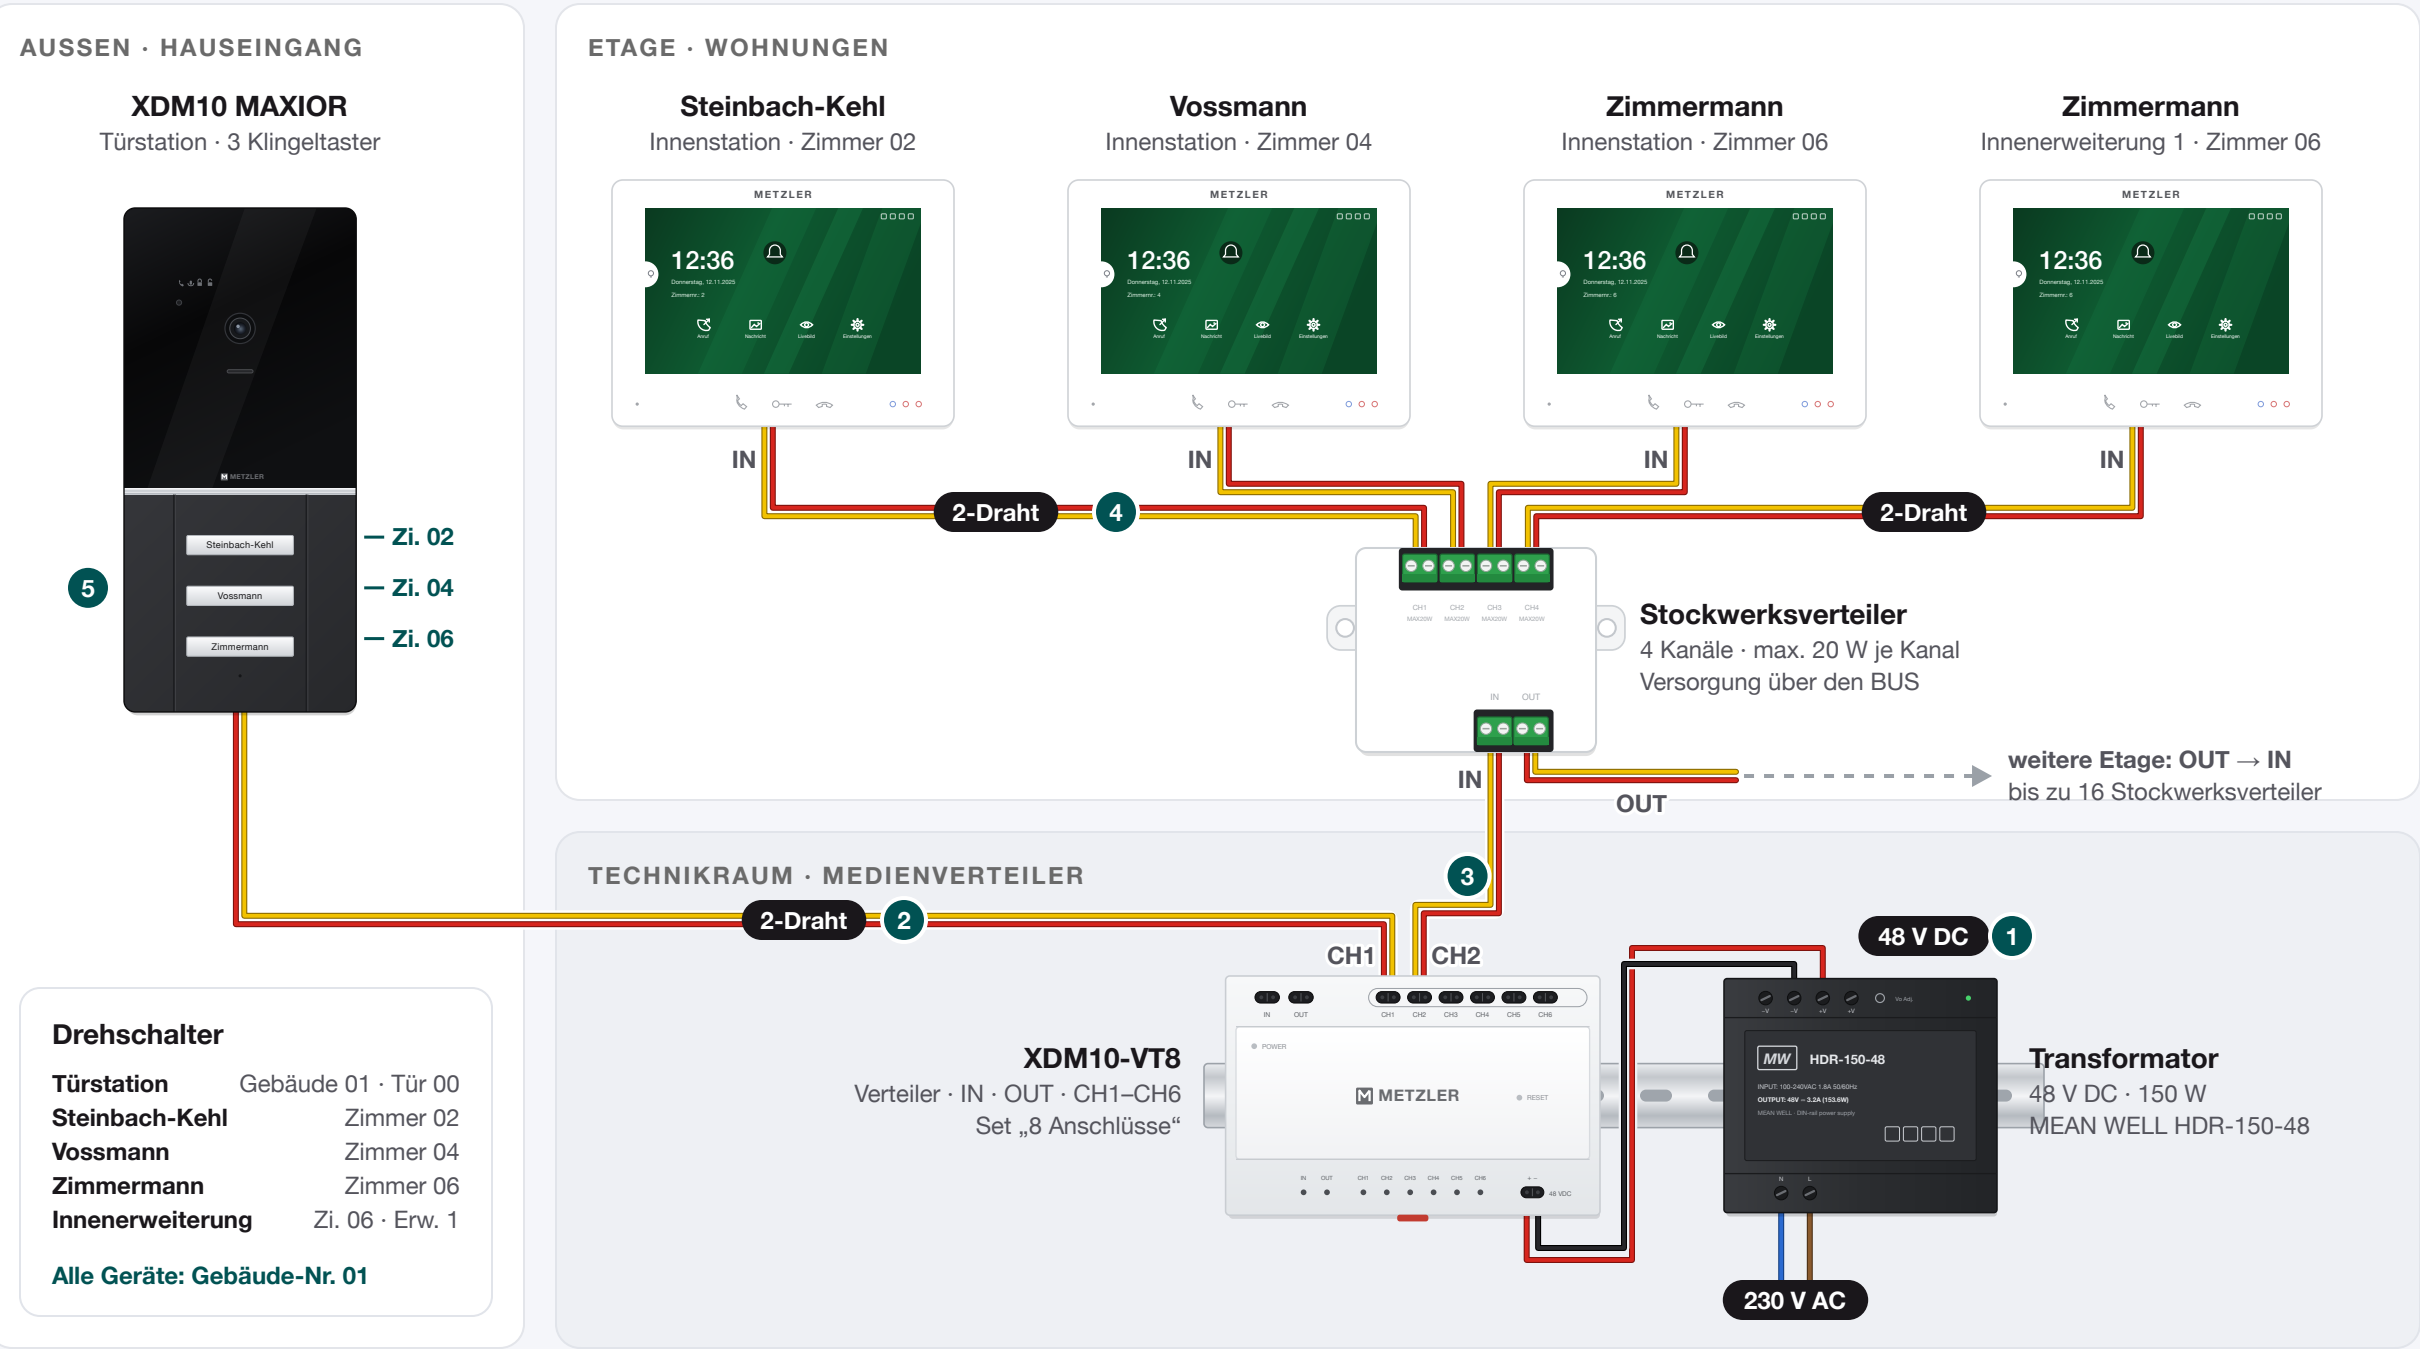

- ### So wird angeschlossen
- 1 Transformator 48 V DC an 230 V anschließen und mit „+ – 48 VDC“ am Verteiler verbinden.
 - 2 Türstation an einen Kanal des Verteilers anschließen (hier CH1).
 - 3 Stockwerksverteiler: Eingang IN an einen weiteren Kanal (hier CH2) – ohne eigenes Netzteil.
 - 4 Jede Innenstation mit eigenem Aderpaar an CH1–CH4 des Stockwerksverteilers.
 - 5 Zimmer-Nr. je Klingeltaster einstellen: 3 Taster = Zimmer 02 / 04 / 06, Erweiterung auf 1.

- ### Wichtig
- Set „8 Anschlüsse“ (Verteiler + 48-V-Transformator 150 W) für Anlagen mit mehr als 4 Innenstationen.
 - Bis zu 16 Stockwerksverteiler pro Gebäude kaskadierbar (OUT → IN).
 - Pro Gerät ein eigenes Aderpaar, keine Netzwerkkabel verwenden.
 - Leitungslängen: Verteiler → Türstation ≤ 60 m; Verteiler → Innenstation ≤ 60 m (Twisted Pair ≤ 40 m).
 - 230-V-Leitungen ≥ 0,5 m entfernt verlegen. Verteiler im Medienverteiler montieren.

- ### Leitungen
- 2-Draht-BUS – 1 Aderpaar je Gerät, z. B. J-Y(St)Y 2x2x0,8
 - 48 V DC · rot = +, schwarz = –
 - 230 V AC · L braun, N blau (Elektrofachkraft)
- ### Klingeltaster → Zimmer-Nr. (XDM10)
- 1 Taster: 03
2 Taster: 02 · 04
3 Taster: 02 · 04 · 06